

ADDENDUM NO. 1 | GLENN CDJR

DATE: 07.10.26

PROJECT: GLENN CDJR
6424 KY-146
CRESTWOOD, KY 40014

OWNER: GLENN CDJR

ARCHITECT: KEYES ARCHITECTS

CIVIL ENGINEER: LAND DESIGN & DEVELOPMENT, INC.

OWNER'S REP: TALLYCM
8715 E. VIA DE COMMERCIO
SCOTTSDALE, AZ 85258

ADDENDUM NO. 1:

This Addendum becomes as fully a part of the previously issued Bid Package as if originally issued therewith or originally contained therein. The Addendum embraces additions to, deductions from, changes and substitutions in, or clarification and emphasis on parts or requirements of the drawings and specifications pertaining to all trades herewith mentioned. Contractors for each trade or contract shall familiarize themselves with Addendum items for all trades and contracts, and they shall be held responsible for complete knowledge of same.


1. Clarification. The due date for Questions/RFI's is Wednesday, July 15, 2026 at 4:00 PM EST.
2. Clarification. Refer to attached Landscape Plan Sheet 1 of 1 dated 5/14/26.

GENERAL LANDSCAPE NOTES:

- ALL PLANT MATERIALS PROPOSED TO MEET LANDSCAPING REQUIREMENTS SHALL BE LIVING PLANTS. PLANTS FROM THE SAME PLANT CATEGORY (TREES, SHRUBS OR VINES) MAY BE SUBSTITUTED FOR PLANTS AS SHOWN ON THE APPROVED PLAN, AS LONG AS THE SUBSTITUTED PLANT IS SIMILAR TO THE APPROVED PLANT IN REGARD TO ITS SIZE AND THE OPAQITY IT PROVIDES. THE APPROVAL BY THE COMMISSION STAFF SHALL BE NECESSARY IN ORDER TO CHANGE PLANTS FROM ONE CATEGORY TO ANOTHER, AND THIS CHANGE MUST BE REFLECTED ON A REVISED PLAN OR IN A CHANGE ORDER SUBMITTED TO THE COMMISSION.
- PLANT MATERIALS USED IN CONFORMANCE WITH PROVISIONS OF THE OLDHAM COUNTY LANDSCAPING REGULATIONS SHALL CONFORM TO THE STANDARDS OF THE AMERICAN STANDARD FOR NURSERY STOCK AND SHALL HAVE PASSED ANY INSPECTIONS REQUIRED UNDER STATE REGULATIONS.
- ALL LANDSCAPE MATERIALS SHALL BE INSTALLED IN A SOUND, PROFESSIONAL MANNER. ALL UNHEALTHY OR DEAD PLANT MATERIAL REQUIRED TO BE PLANTED OR PRESERVED SHALL BE REPLACED WITHIN ONE YEAR, OR BY THE NEXT PLANTING PERIOD, WHICHEVER COMES FIRST.
- NO TREE SHALL BE PLANTED CLOSER THAN 5 FEET TO ANY FIREPLUG, UTILITY POLE OR SIMILAR UTILITY STRUCTURE. PLANTS MUST BE SPECIFIED, LOCATED, AND MAINTAINED SO AS TO NOT INTERFERE WITH PUBLIC UTILITIES. ULTIMATE DETERMINATION OF SAID POTENTIAL INTERFERENCE AND IDENTIFICATION OF ANY REMEDIAL SPECIFICATION OF PLANTINGS VESTS IN THE LANDSCAPE CONSULTANT.
- NO TREE SHALL BE PLANTED IN A SPACE EQUAL TO OR LESS THAN 3 FEET IN WIDTH.
- GROUND COVERS, OTHER THAN GRASS, USED SHALL BE INSTALLED IN SUCH A MANNER AS TO PRESENT A FINISHED APPEARANCE AND COMPLETE COVERAGE WITHIN THREE (3) YEAR OF PLANTING.
- GRASS AREAS MAY BE SODDED, PLUGGED, SPRIGGED OR SEEDED AND SHALL PRESENT A UNIFORM HEALTHY STAND OF THE SPECIFIED GRASSES FOLLOWING THE FIRST FULL GROWING SEASON AFTER INSTALLATION.
- ANY TREE THAT IS NOT NURSERY STOCK AND IS TO BE MOVED IN ORDER TO MEET REQUIREMENTS OF THIS REGULATION SHALL BE TRANSPLANTED IN ACCORDANCE WITH SOUND PLANTING GUIDELINES ADEQUATE TO SUSTAIN VIGOROUS AND HEALTHY GROWTH.
- ANY LANDSCAPE MATERIALS, INCLUDING GRASSES, WHICH FAIL TO MEET THE MINIMUM APPROVED REQUIREMENTS AT TIME OF INSTALLATION, AS SET FORTH IN THIS DIVISION, SHALL BE REMOVED AND REPLACED WITH ACCEPTABLE MATERIALS.
- FOR SITES THAT ARE GREATER THAN TWO (2) ACRES IN SIZE, PLANT MATERIAL THAT IS CHOSEN TO FULFILL THE REQUIREMENT OF THIS DIVISION SHALL NOT EXCEED A MAXIMUM AMOUNT OF 50% OF ONE SPECIES.

PLANT SCHEDULE									
TREES									
KEY	QTY.	BOTANICAL NAME	COMMON NAME	INSTALLATION SIZE	MATURE SIZE	ROOT	REMARKS		
GT	8	GLEDTISIA TRIACANTHUS VAR. INERMIS 'SHADEMASTER'	SHADEMASTER HONEY LOCUST	1 3/4" CAL.	45/70' HT. & 25/35' SPREAD	B&B	TYPE "A" TREE (0)		
ZS	5	ZELKOVA SERRATA	JAPANESE ZELKOVA	1 3/4" CAL.	50/80' HT. & 50/75' SPREAD	B&B	TYPE "A" TREE (0)		
EU	5	EUCOMMIA ULMOIDES (MALE ONLY)	HARDY RUBBER TREE	1 3/4" CAL.	40/60' HT. & 30/50' SPREAD	B&B	TYPE "B" TREE (0)		

PROPERTY LINE/CURVE TABLE			
L1	S19°13'43"W	15.81'	R=8,111.94'
L2	S19°32'36"W	24.28'	R=6,510.82'
L3	S19°58'19"W	24.23'	R=5,440.64'
L4	S20°23'09"W	8.00'	R=4,671.31'
L5	S20°32'03"W	16.18'	R=4,671.31'
L6	S21°04'54"W	24.13'	R=4,091.60'
L7	S21°45'45"W	24.09'	R=4,074.98'
L8	S22°23'27"W	8.75'	R=5,466.47'
L9	S22°31'34"W	17.06'	R=5,466.47'
L10	N27°35'57"E	29.83'	

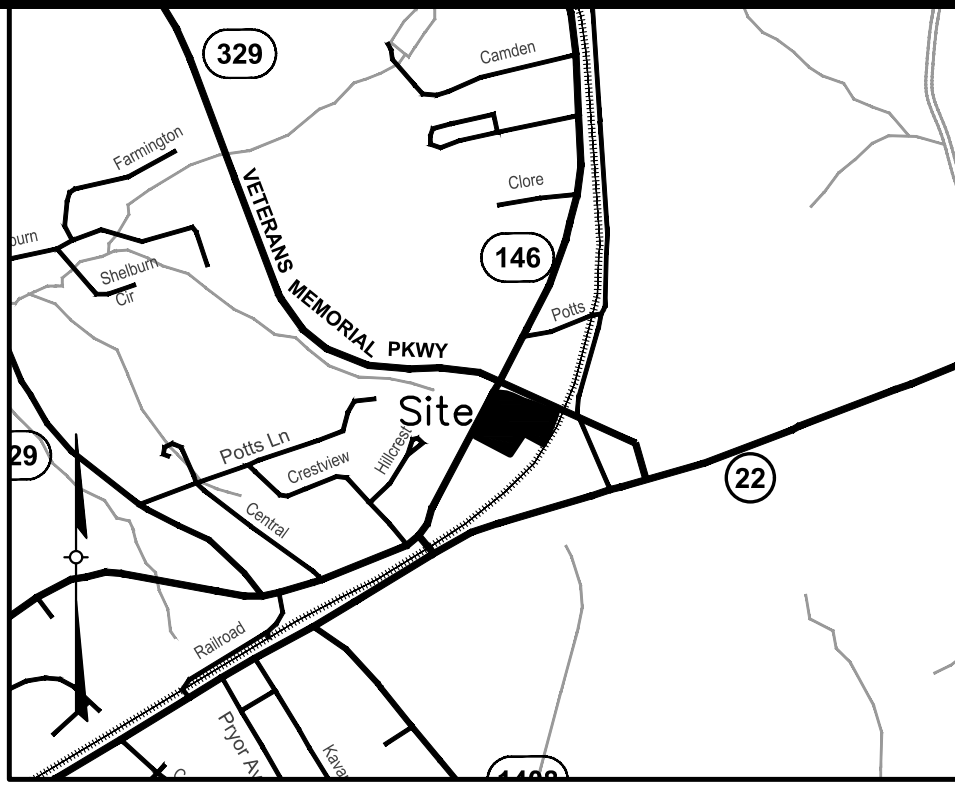

LOCATION MAP
NOT TO SCALE

SITE DATA

TRACT 1

SITE AREA	= 3.6± Ac. (179,937 SF)
EXISTING ZONING	= C-3
EXISTING USE	= MOTOR VEHICLE SALES
PROPOSED USE	= MOTOR VEHICLE SALES
BUILDING HEIGHT	= 25'
BUILDING AREA	= 32,886 SF

LOT COVERAGE STRUCTURES	= 32,886 SF (18%)
-------------------------	-------------------

F.A.R.	= 0.18
--------	--------

PARKING REQUIRED


	MIN.	MAX.
MOTOR VEHICLE SALES		
1 SP/7,000 SF OF OUTDOOR SALES (27,089 SF)	= 4 SP	
1 SP/5,000 SF OF OUTDOOR SALES (27,089 SF)		6 SP
1 SP/250 SF OF INDOOR SALES (5,315 SF)	= 22 SP	
1 SP/150 SF OF INDOOR SALES (5,315 SF)		36 SP
1 SP/EMPLOYEE (10 EMPLOYEES) + 2 SP/SERVICE BAY (18 BAYS)	= 46 SP	
1 SP/EMPLOYEE (10 EMPLOYEES) + 5 SP/SERVICE BAY (18 BAYS)		100 SP
TOTAL PARKING REQUIRED	= 72 SP	142 SP

PARKING PROVIDED	
CUSTOMER PARKING	= 18 SPACES (2 HC SP INCLUDED)
EMPLOYEE PARKING	= 15 SPACES
SERVICE PARKING	= 23 SPACES
SERVICE BAY PARKING (18 SERVICE BAYS)	= 18 SPACES
TOTAL PARKING PROVIDED (CUSTOMER/EMPLOYEE/SERVICE)	= 74 SPACES (2 HC SP INCLUDED)

TOTAL DISPLAY SPACES	= 137 SPACES
----------------------	--------------

VEHICULAR USE AREA	= 107,788 SF
INTERIOR LANDSCAPE AREA REQUIRED	= 5,389 SF (LA=5 SF/100 SF V.U.A.)
INTERIOR LANDSCAPE AREA PROVIDED	= 5,972 SF
ILA TREES REQUIRED	= 22 TREES (VUA REQ./250 SF)
ILA TREES PROPOSED	= 22 TREES

EXISTING IMPERVIOUS	= 155,947 SF (86.7%)
PROPOSED IMPERVIOUS	= 141,466 SF (78.6%)

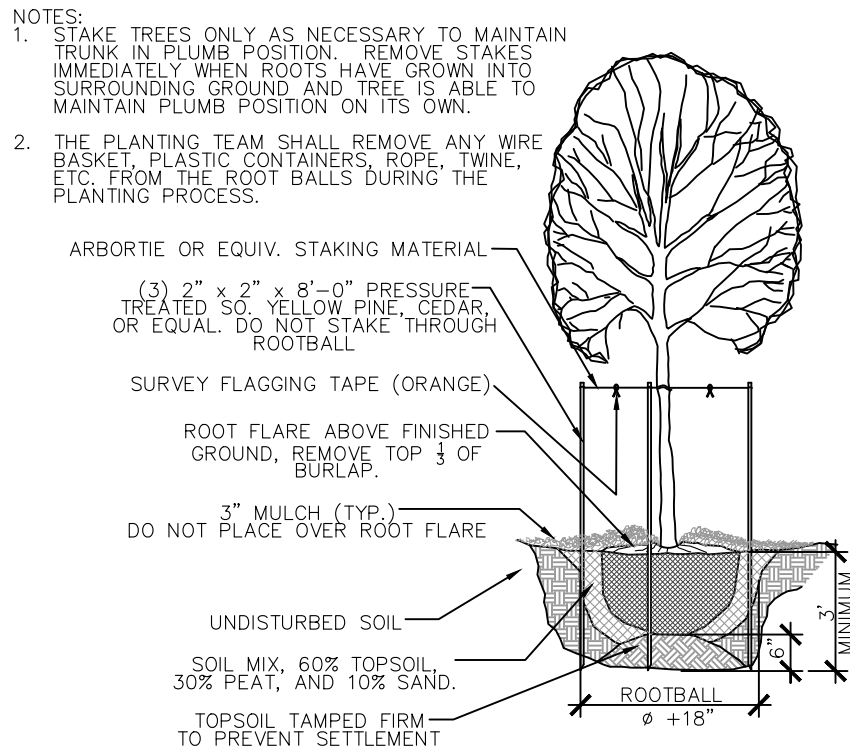


TYPICAL TREE PLANTING & STAKING
N.T.S.

SITE ADDRESS:
6426 W HWY 146
CRESTWOOD, KY 40014
24-C.2-02-15A
TAX BLOCK 04 CRESTWOOD, LOT 15A
D.B. 1275, PG. 268

SITE ADDRESS:
6424 W HWY 146
CRESTWOOD, KY 40014
24-C.2-02-16&17
TAX BLOCK 04 CRESTWOOD, LOT 16 & 17
D.B. 1368, PG. 460

OWNER:
GLENN LOUISVILLE CDJR RE LLC
2036 SURREY LN
LAS VEGAS, NEVADA 89119


UTILITY NOTE: ALL UTILITIES SHOWN ON THESE PLANS ARE APPROXIMATE. THE INDIVIDUAL SERVICE LINES ARE NOT SHOWN. THE CONTRACTOR OR SUBCONTRACTOR SHALL NOTIFY THE UTILITY PROTECTION CENTER, KENTUCKY 811 (TOLL FREE PHONE NO. 1-800-752-6007 OR LOCAL NO. 502-266-5123) FORTY EIGHT HOURS IN ADVANCE OF ANY CONSTRUCTION ON THIS PROJECT. THIS NUMBER WAS ESTABLISHED TO PROVIDE ACCURATE LOCATIONS OF EXISTING BELOW GROUND UTILITIES (I.E. CABLES, ELECTRIC WIRES, GAS, AND WATERLINES). WHEN CONTACTING THE KENTUCKY 811 CALL CENTER, PLEASE STATE THAT THE WORK TO BE DONE IS FOR A PROPOSED MSD SEWER OR DRAINAGE FACILITY. THE CONTRACTOR SHALL BE RESPONSIBLE FOR BECOMING FAMILIAR WITH ALL UTILITY REQUIREMENTS SET FORTH ON THE PLANS IN THE TECHNICAL SPECIFICATIONS AND SPECIAL PROVISIONS.

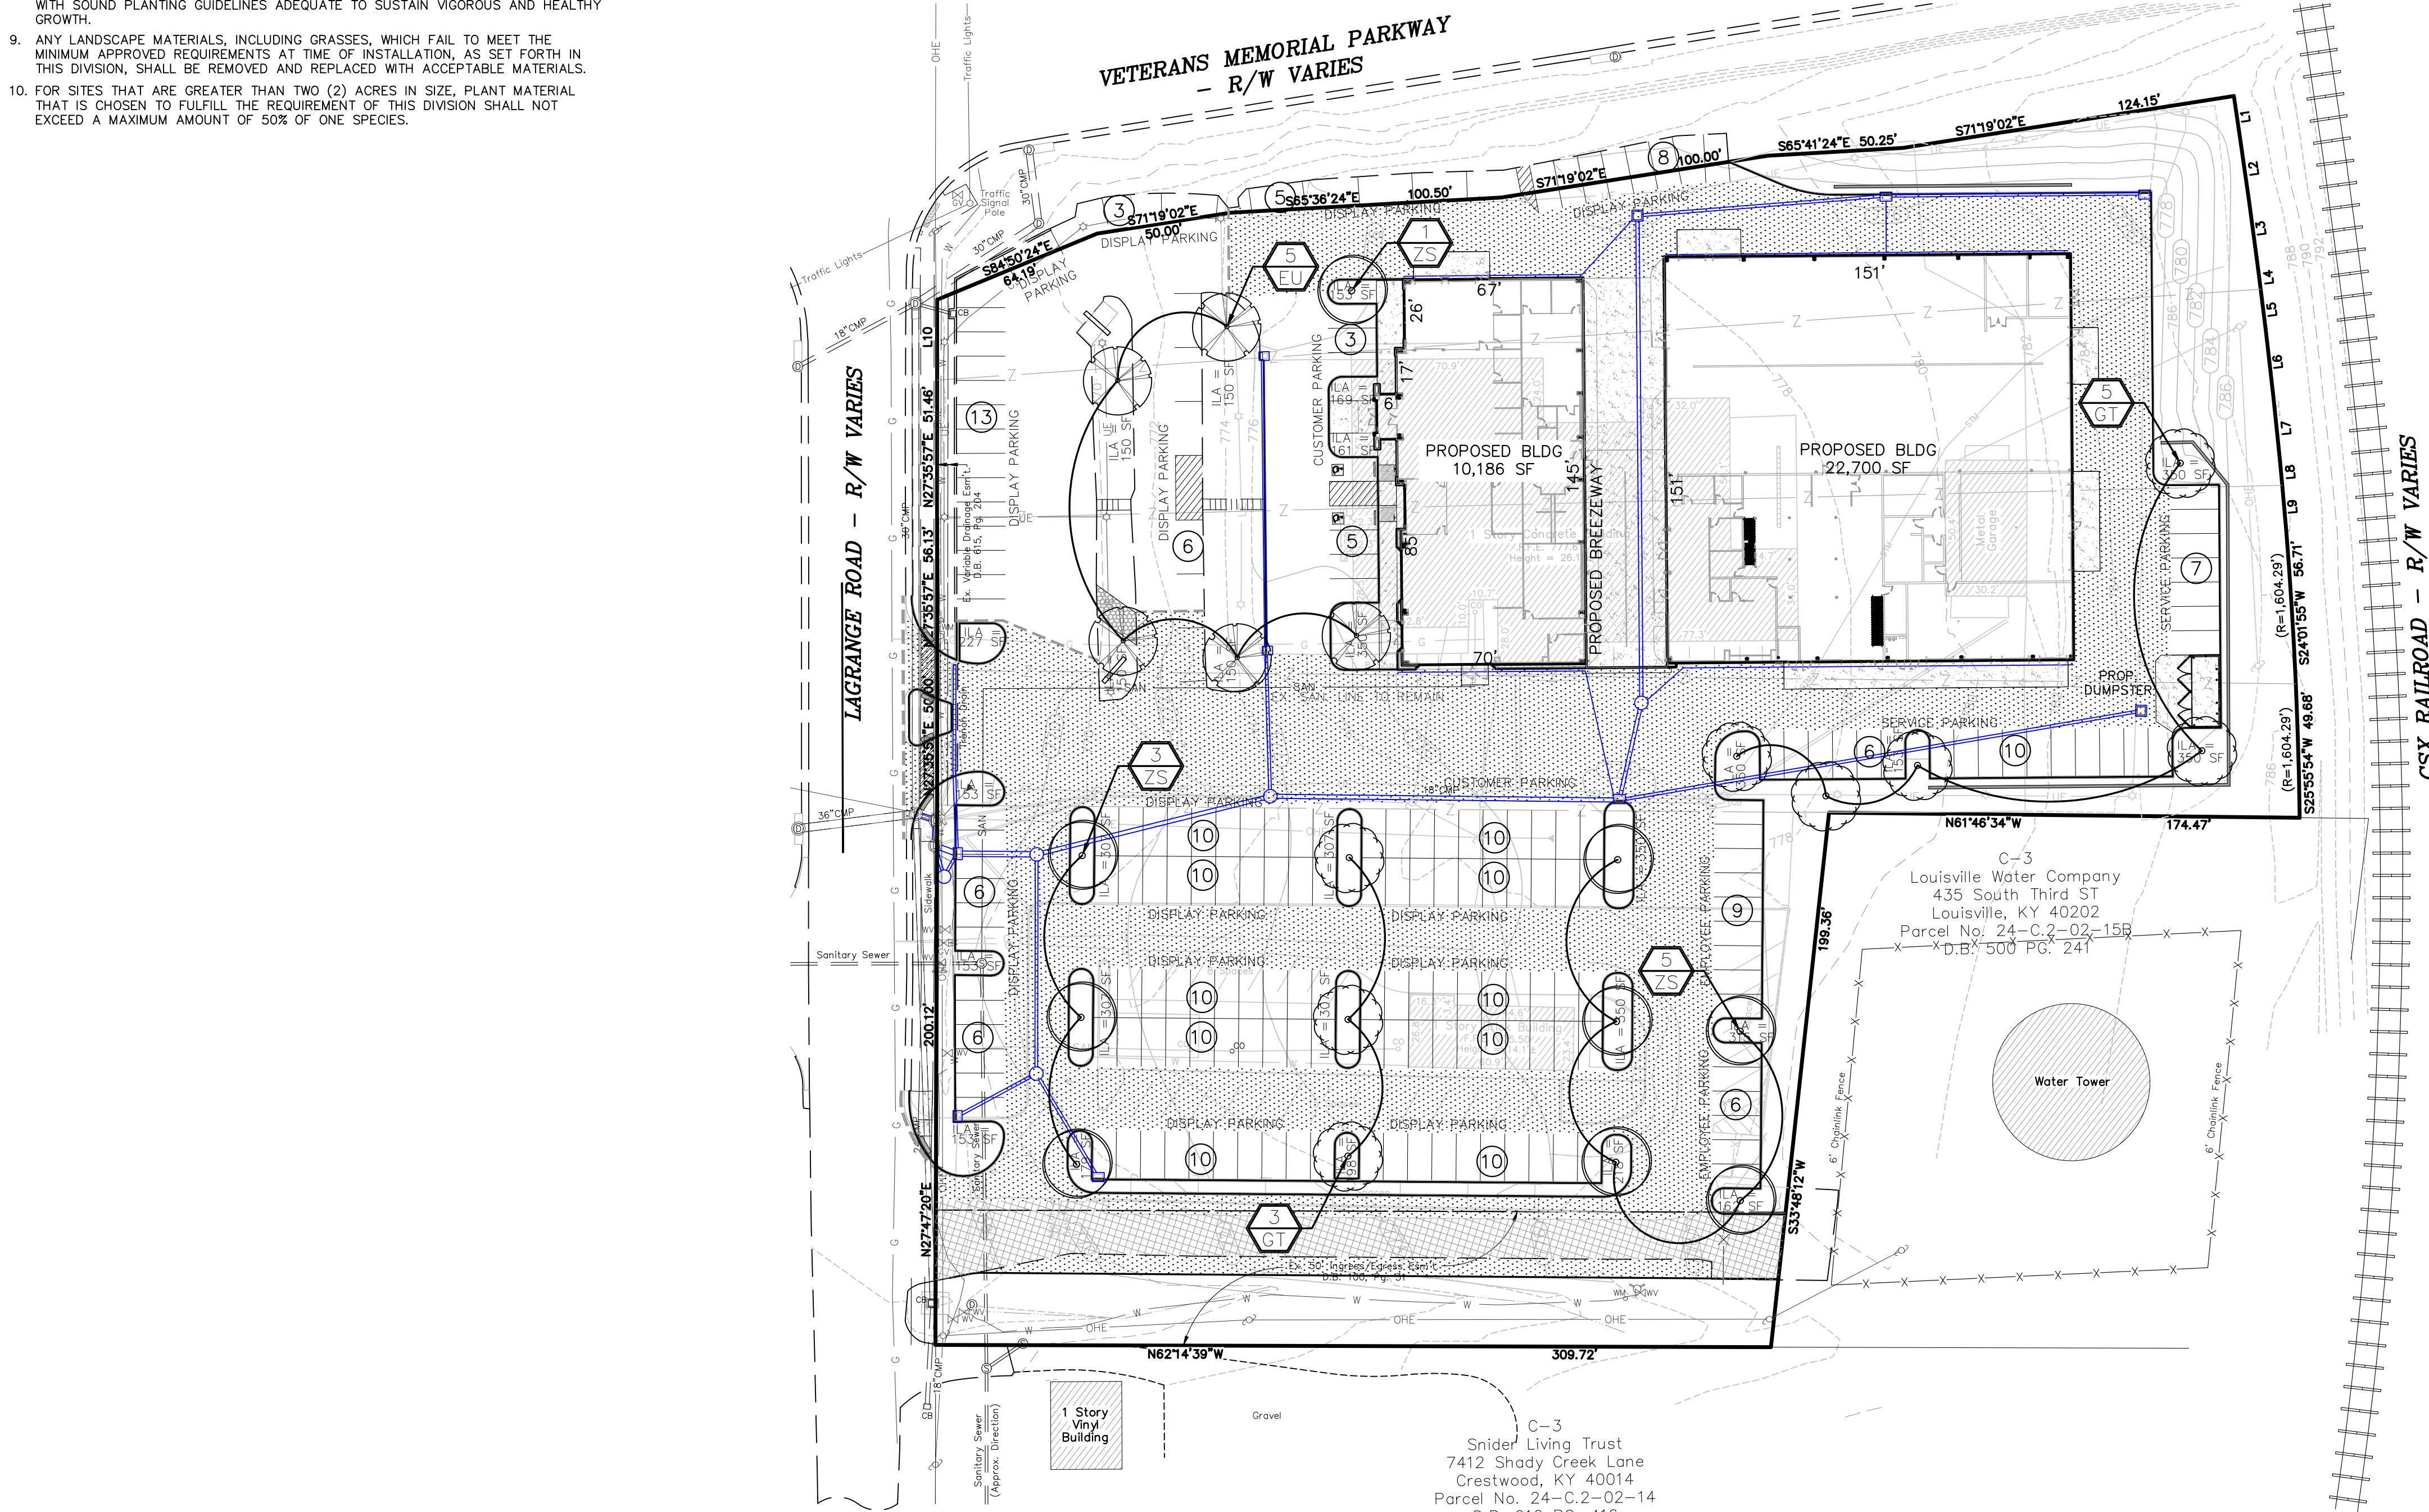

LEGEND

- PROPOSED STORM SEWER
- EXISTING CONTOUR
- EXISTING STORM SEWER
- EXISTING SEWER AND MANHOLE
- EXISTING SANITARY SEWER
- EXISTING WATER LINES
- EXISTING GAS LINES
- EXISTING OVERHEAD ELETRIC
- EXISTING UNDERGROUND ELECTRICAL
- LIGHT POLE
- EXISTING GUY WIRE
- WATER METER
- EXISTING UTILITY POLE
- EXISTING GAS VALVE
- EXISTING FIRE HYDRANT
- EXISTING WATER VALVE

GRAPHIC SCALE

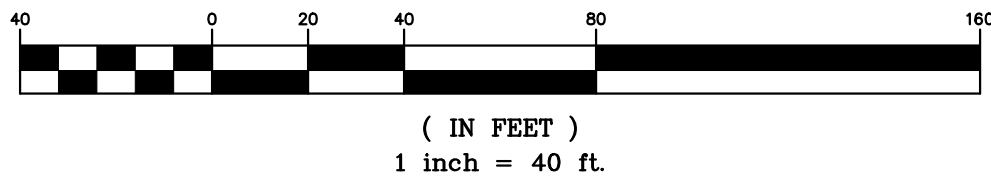

(IN FEET)
1 inch = 40 ft.

REVISIONS	
NO.	DESCRIPTION

PROJECT DATA	
FILE NAME:	25107 - LSCAPE
DATE:	5/14/26
CHECKED BY:	ZS
DRAWN BY:	NK

LANDSCAPE PLAN	
GLENN CDJR	6424 KY-146
OWNER/DEVELOPER	GLENN CDJR
6426 W HWY 146	CRESTWOOD, KY 40014

LAND DESIGN & DEVELOPMENT, INC.	ENGINEERING • LAND SURVEYING • LANDSCAPE ARCHITECTURE
505 WILSON BLVD	505 WILSON BLVD
LAS VEGAS, NV 89101	LAS VEGAS, NV 89101
PHONE: 702.444.9714	FAX: 702.444.9714
WEB SITE: WWW.LDD-INC.COM	

LANDSCAPE PLAN	GLENN CDJR
6424 KY-146	OWNER/DEVELOPER
GLENN CDJR	6426 W HWY 146
CRESTWOOD, KY 40014	

JOB NO.	25107
SHEET	1
OF	1